
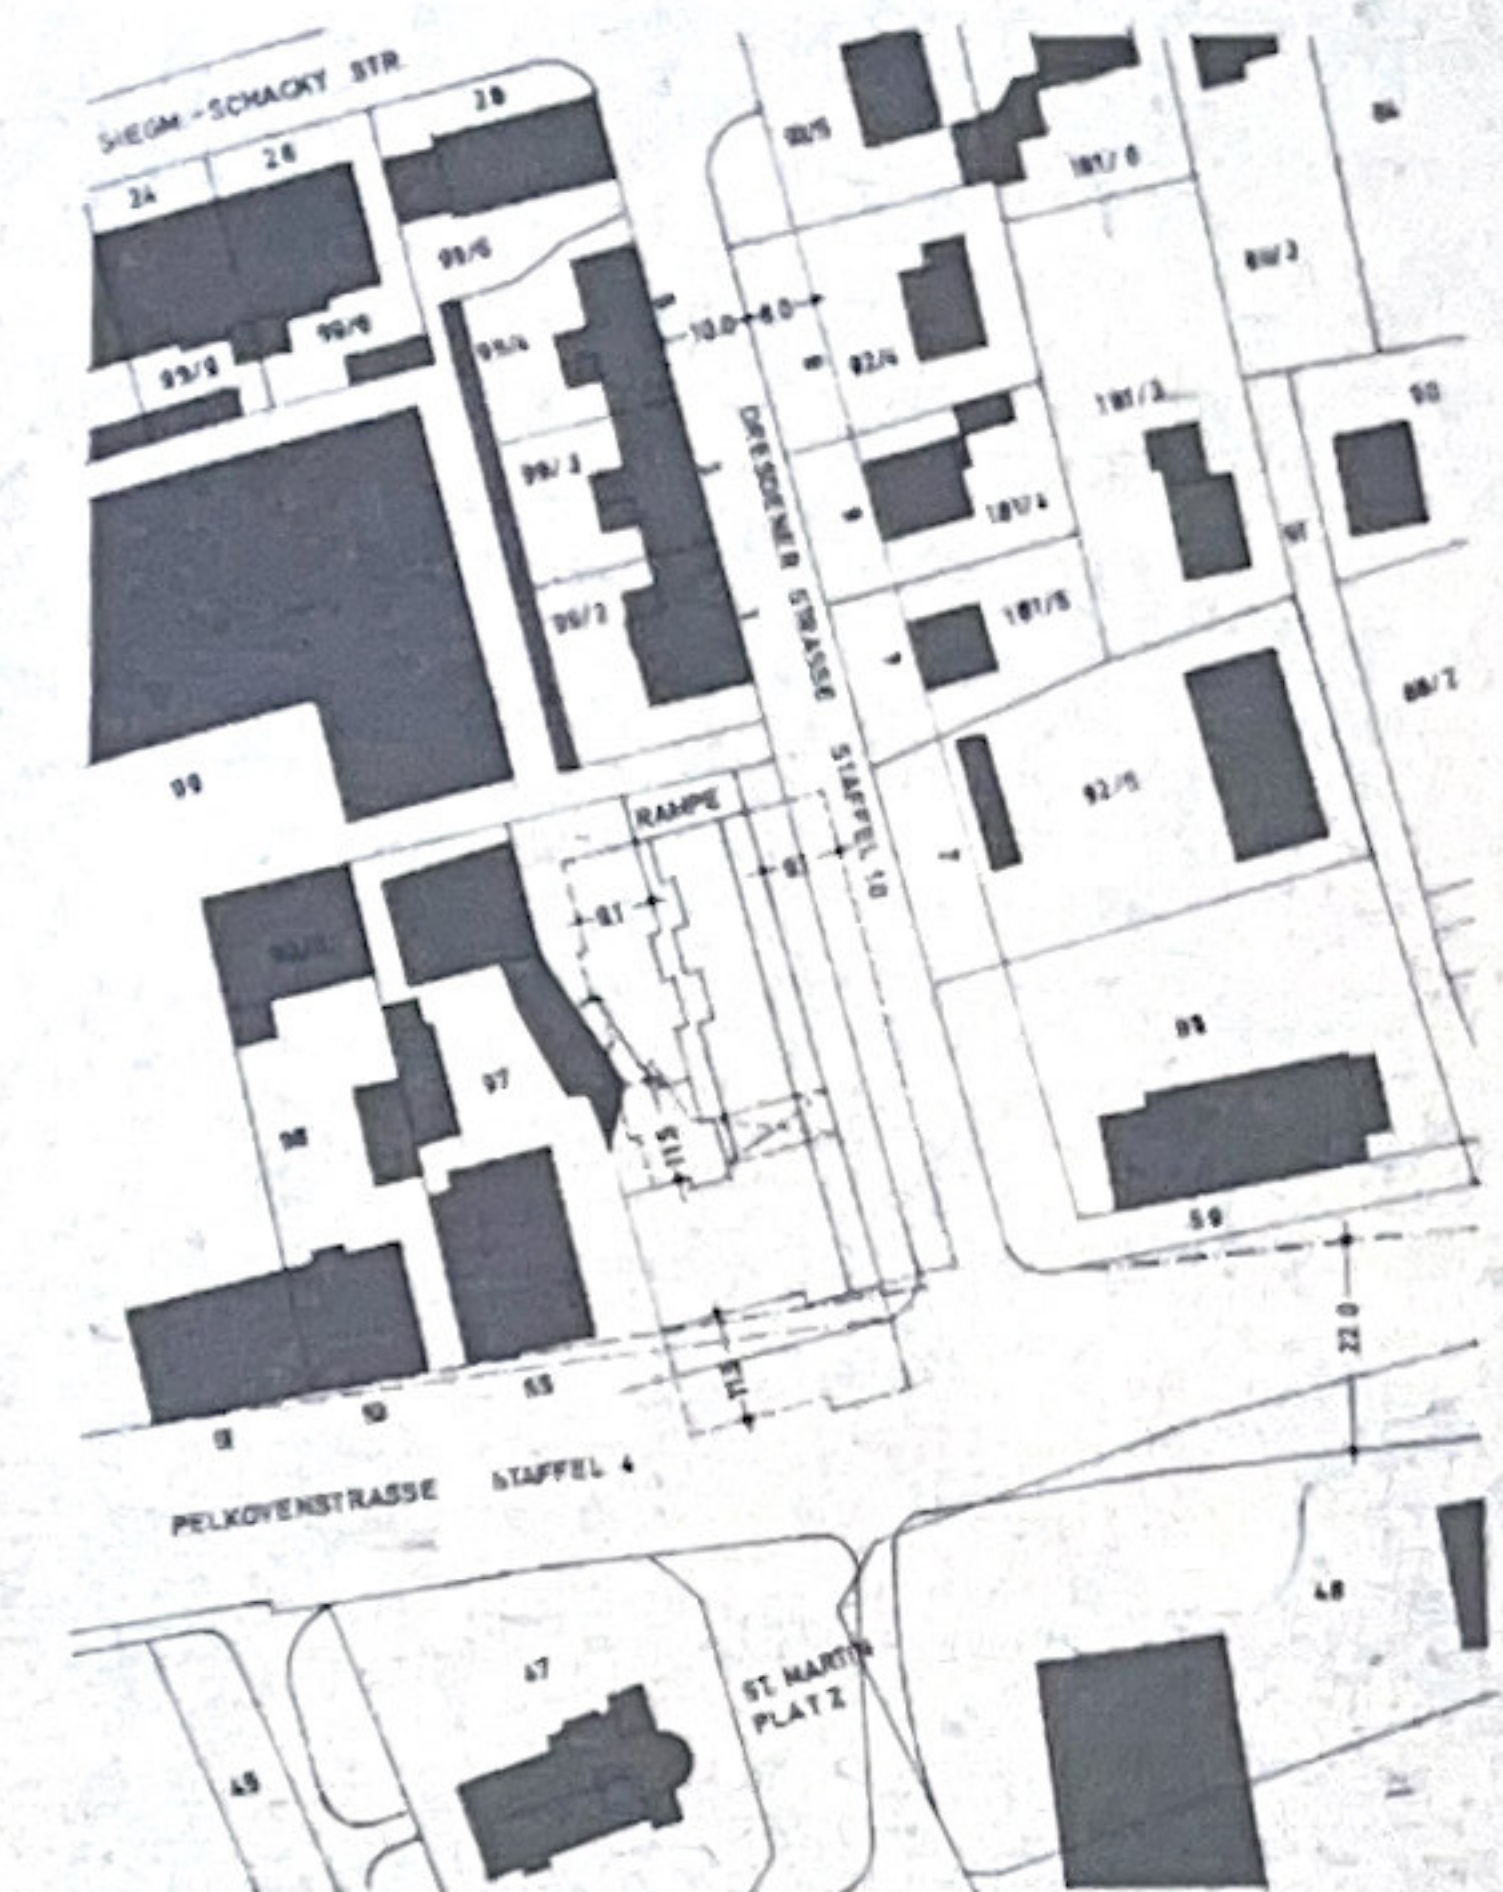


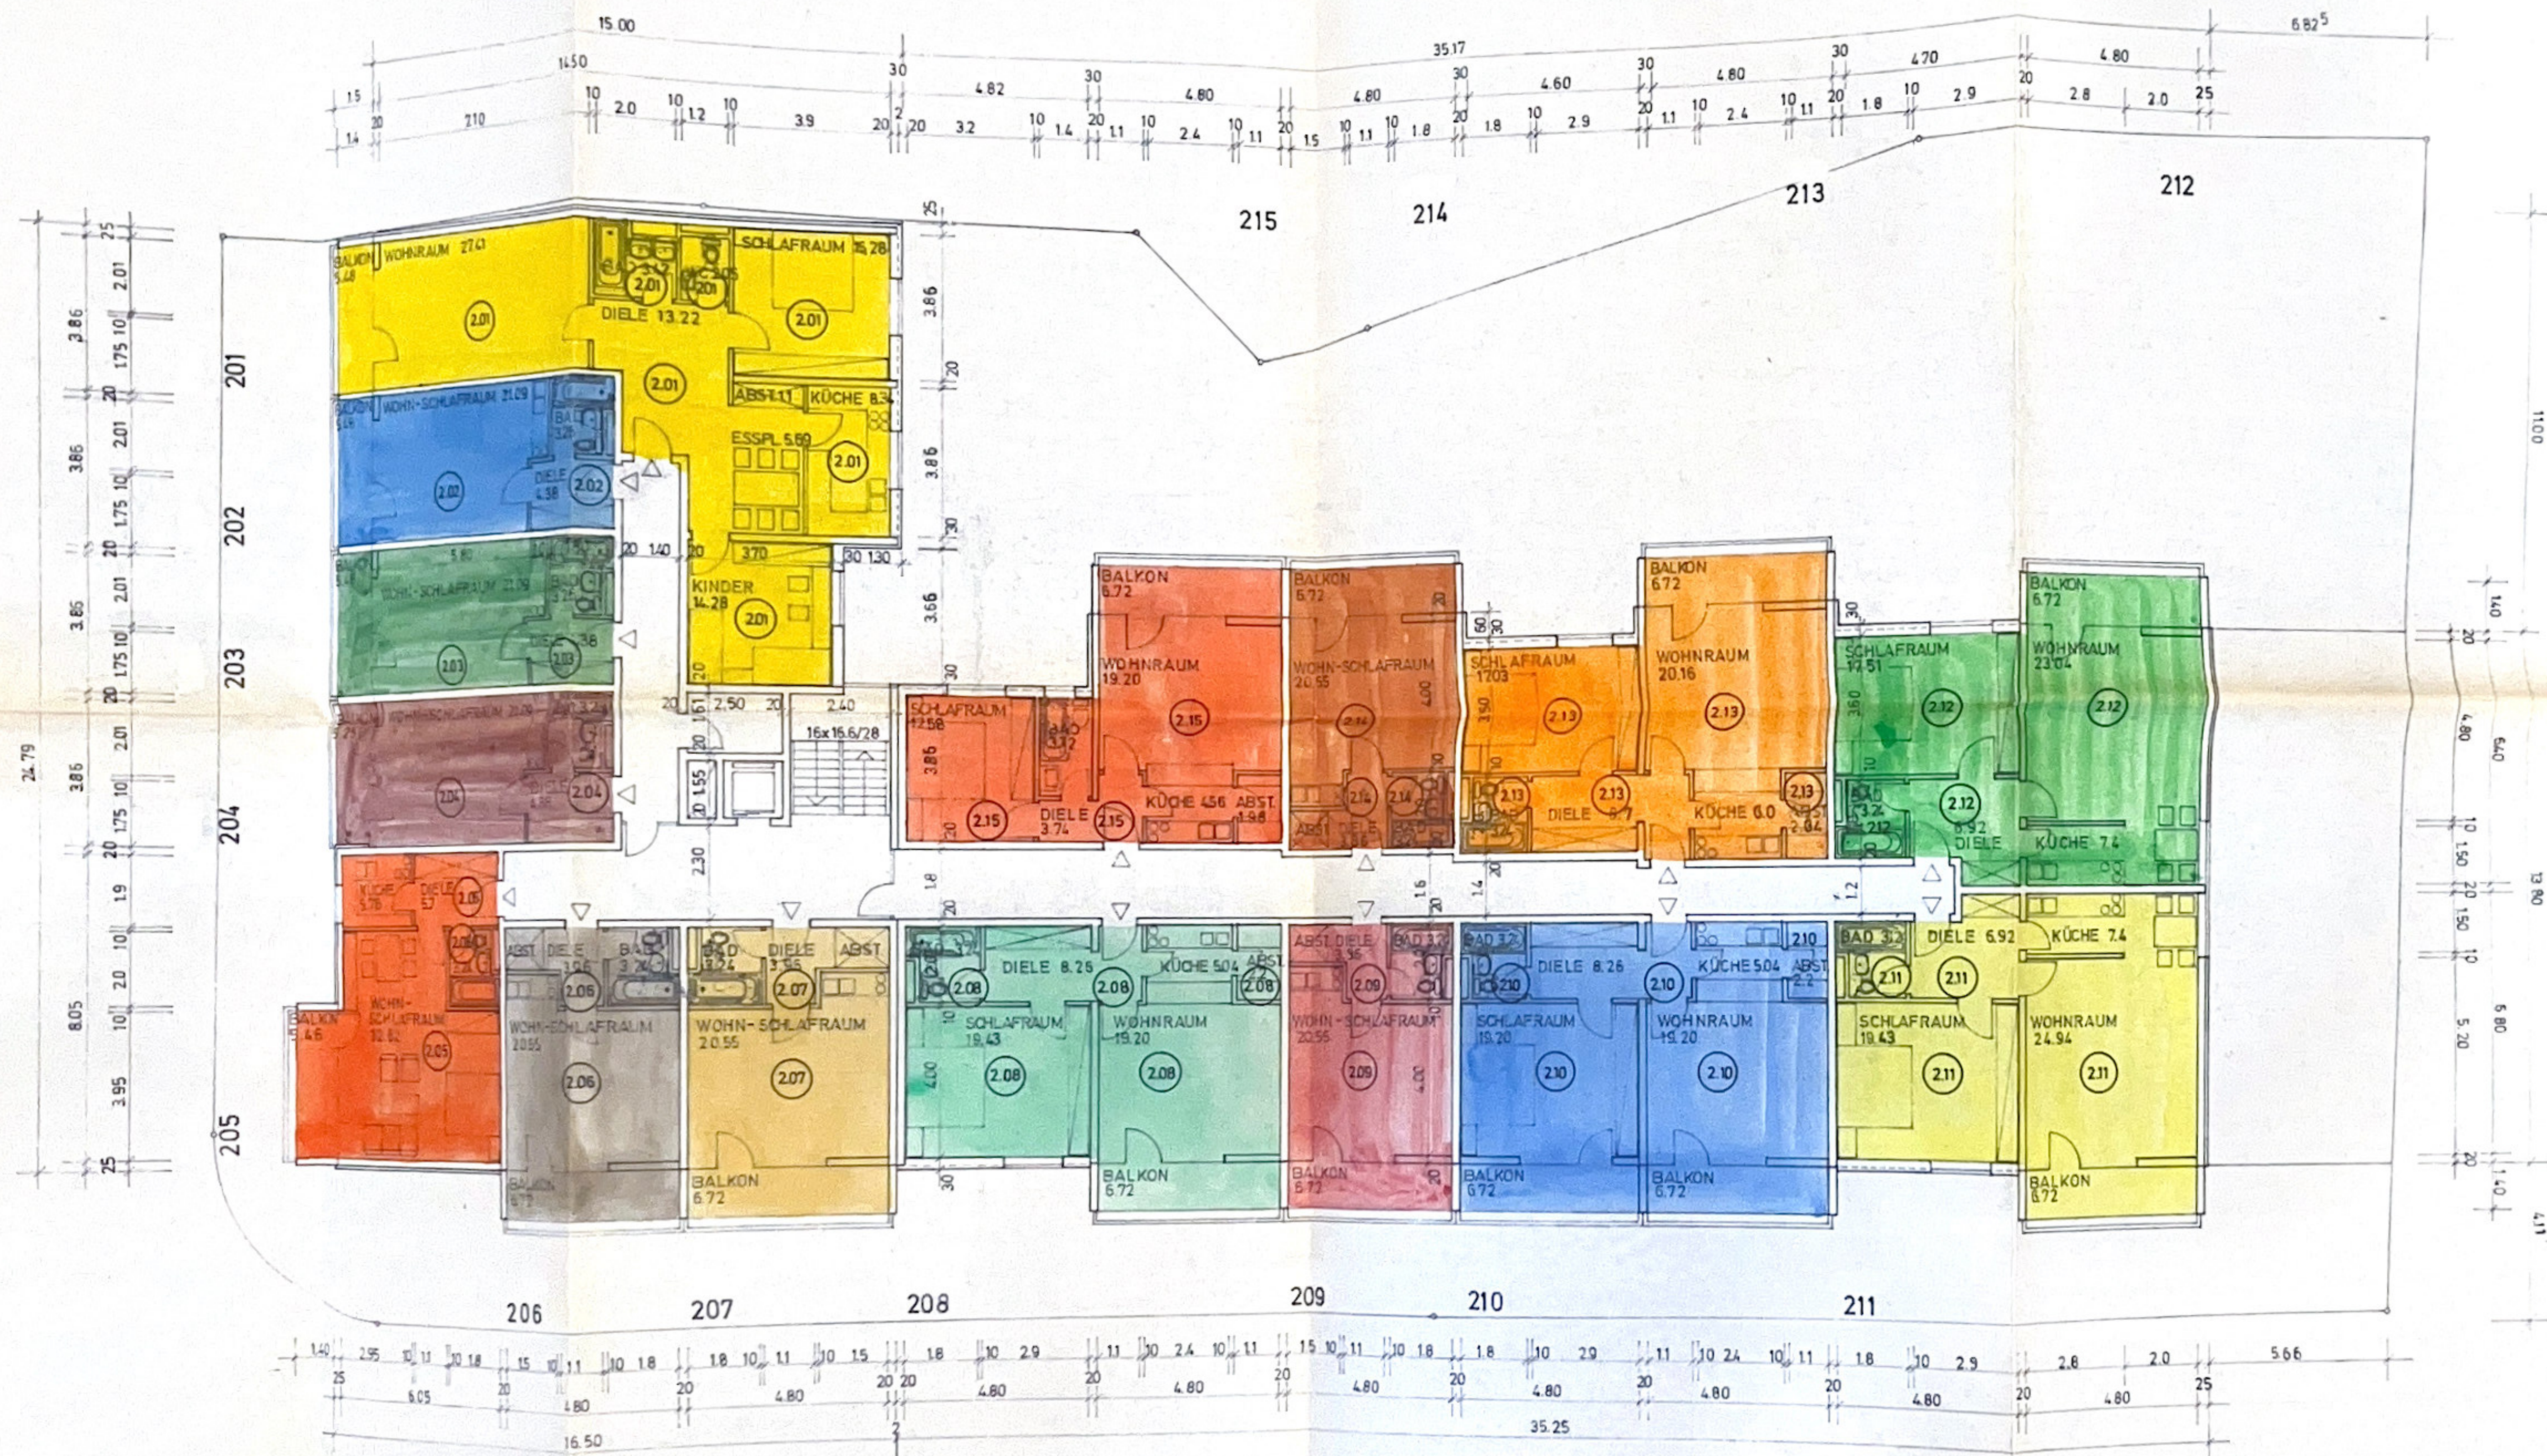

LAGEPLAN M 1:1000

GEMARKUNG MOOSACH
FLURSTÜCK NR. 94
BLATT NR. 954/955

DER BAUHERR UND GRUNDSTÜCKSEIGNER:

DIE NACHBARN:
ZUR KENNNTIS GENOMMEN UND ZUGESTIMMT
FLURSTÜCK-NR. 97

FLURSTÜCK-NR. 99

DIE ARCHITEKTEN:

DIPL. ING. ARCH. G. LUDWIG & F. RAAB, MÜ. 2 - LINPRUNSTR. 49
TELEFON 1952 ER

PROJEKT:
MEHRFAMILIENWOHNHAUS MIT BIERSTUBE
UND TIEFGARAGE
MÜNCHEN-MOOSACH PELKOVENSTRASSE 57
BEZEICHNUNG:
GRUNDRISS
2 OBERGESCHOSS

BAUHERR:
DIPL. ING.
F. RAAB
PLAN NR.
32T

GEZ.	DAF.	GEPR.	MASSSTAB.
KE	8.12.1972		1:100
	16.5.73	TREPPHAUSTUREN	
	22.5.73	TEILUNGSPLAN	

